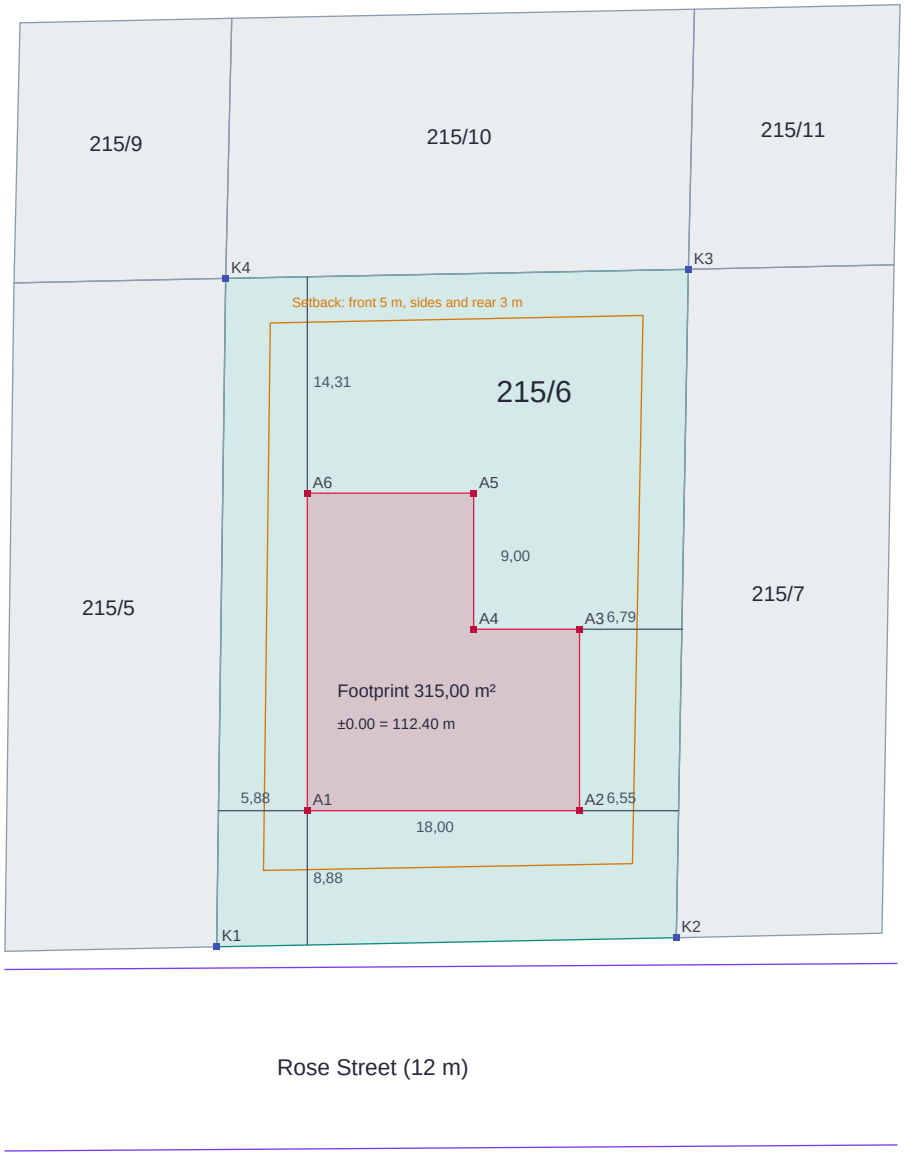

Setting-out plan, block 215 parcel 6

ITRF96 TM30 · Ölçek 1:500 · 28.10.2026

PARCEL
SETBACK
NEIGHBOUR
FOOTPRINT
ROAD
STAKE_OUT
20 m